




DATE		13.03.2019
REVISION		01
DRAWN		2019-09-30
CHECKED		13.03.2019
RELEASER		BOH
SCALE		1:250
PROJECT		Paintshop
SUBJECT		CV-Layout
DRAWING		EG / ±0,00m
DRAWING		SWW Shanghai
DRAWING		CN01-2301765
DRAWING		A11010
DRAWING		20086753
DRAWING		1/1